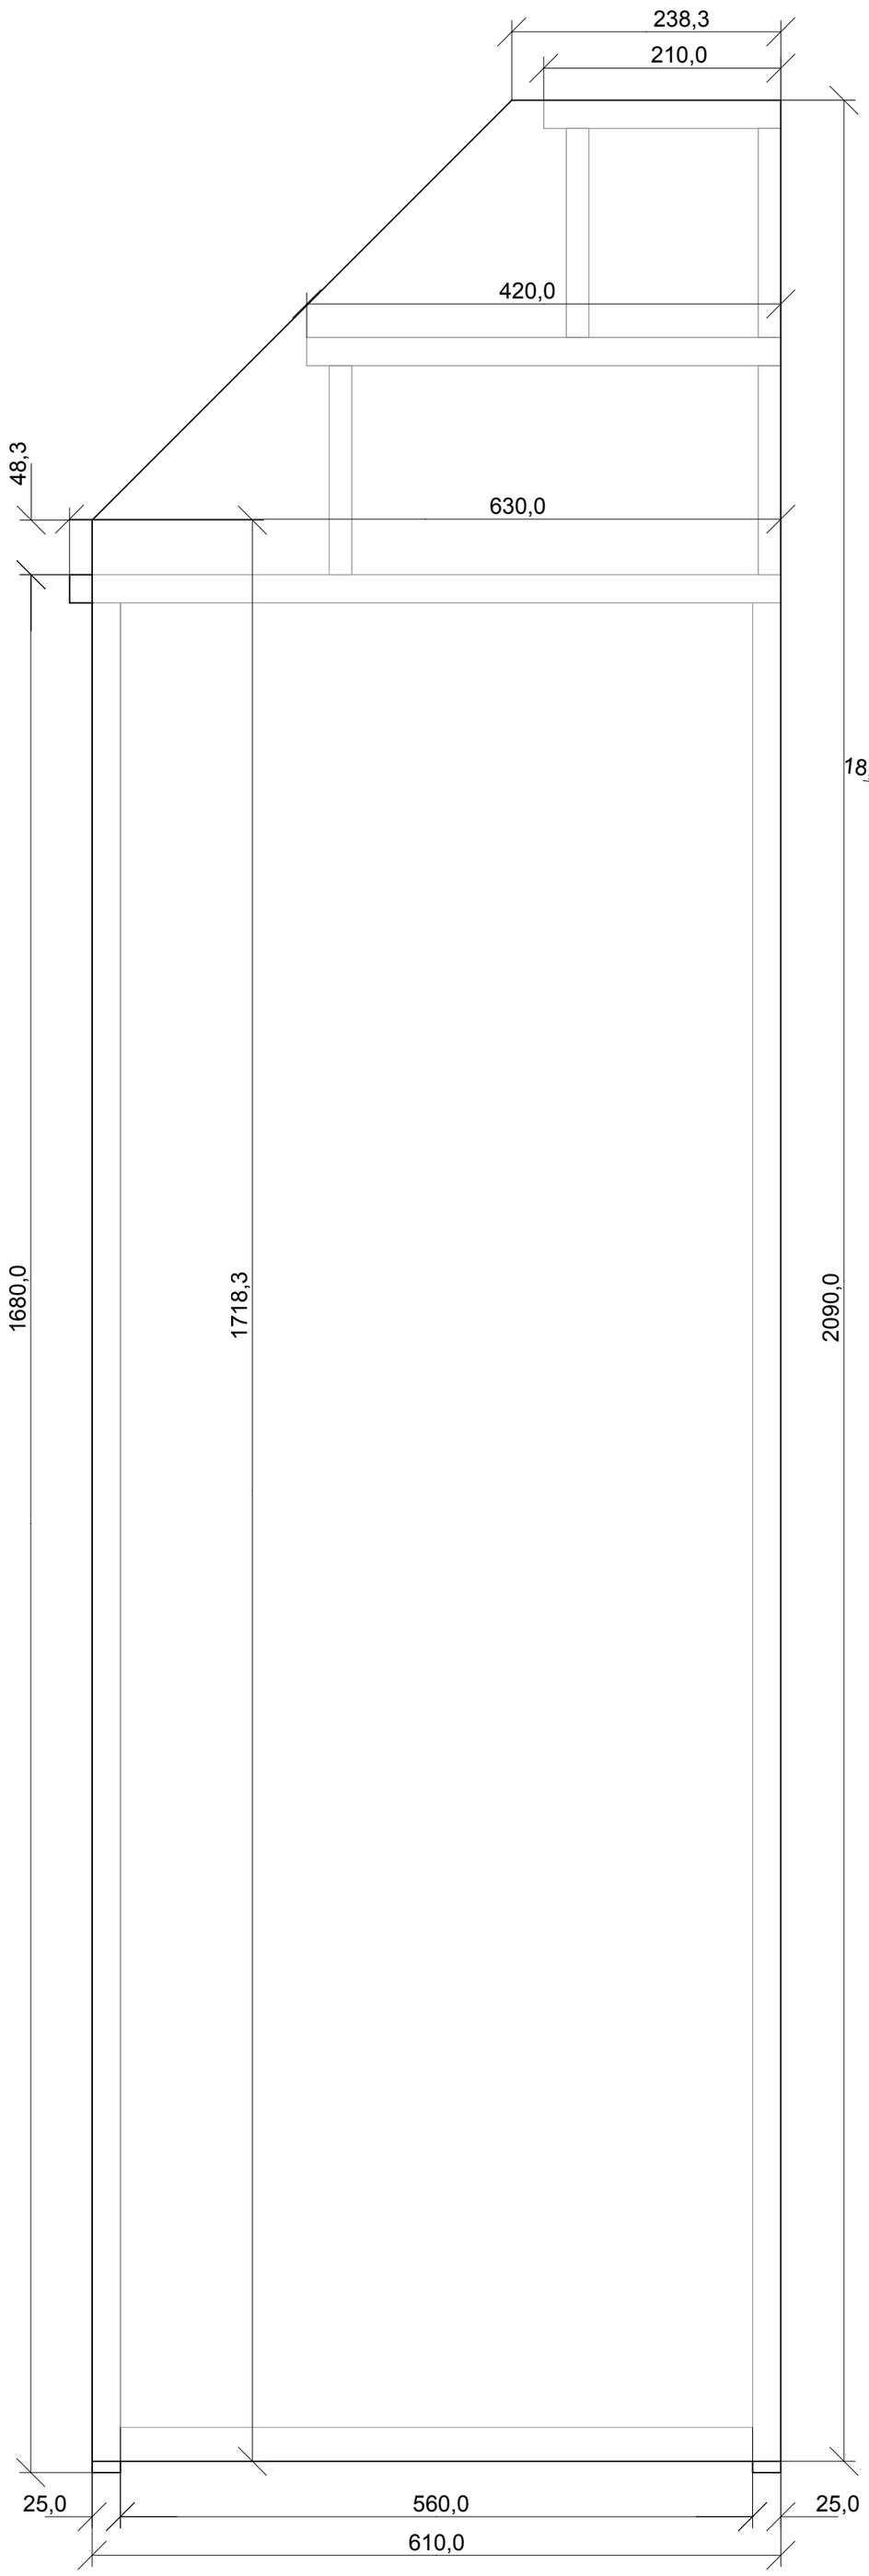

I sistemi di giunzione tra i pannelli ed eventuali rinforzi di irrigidimento saranno da valutare in fase di realizzazione al fine di garantire piena stabilità e adeguata robustezza.
La finitura dell'anta del box sarà indicata successivamente.

MFARCHITETTI

PROGETTO:

CASA VACANZE A SESTRI SCALA INTERNA

LUOGO:

COMMITTENTE:

ARCHITETTI:

MARZIA FILATRELLA
MARCO FERRARA

OGGETTO:

BOX FRIGO

NOTE:

-

NOME FILE:

-

VERS	DATA
A	**2017.04.19**

TAVOLA NO.: **002** DI **002**

A102

DATA: **2017/04/19** SCALA: **1:5**
REV: **A** FORMATO: **A2**